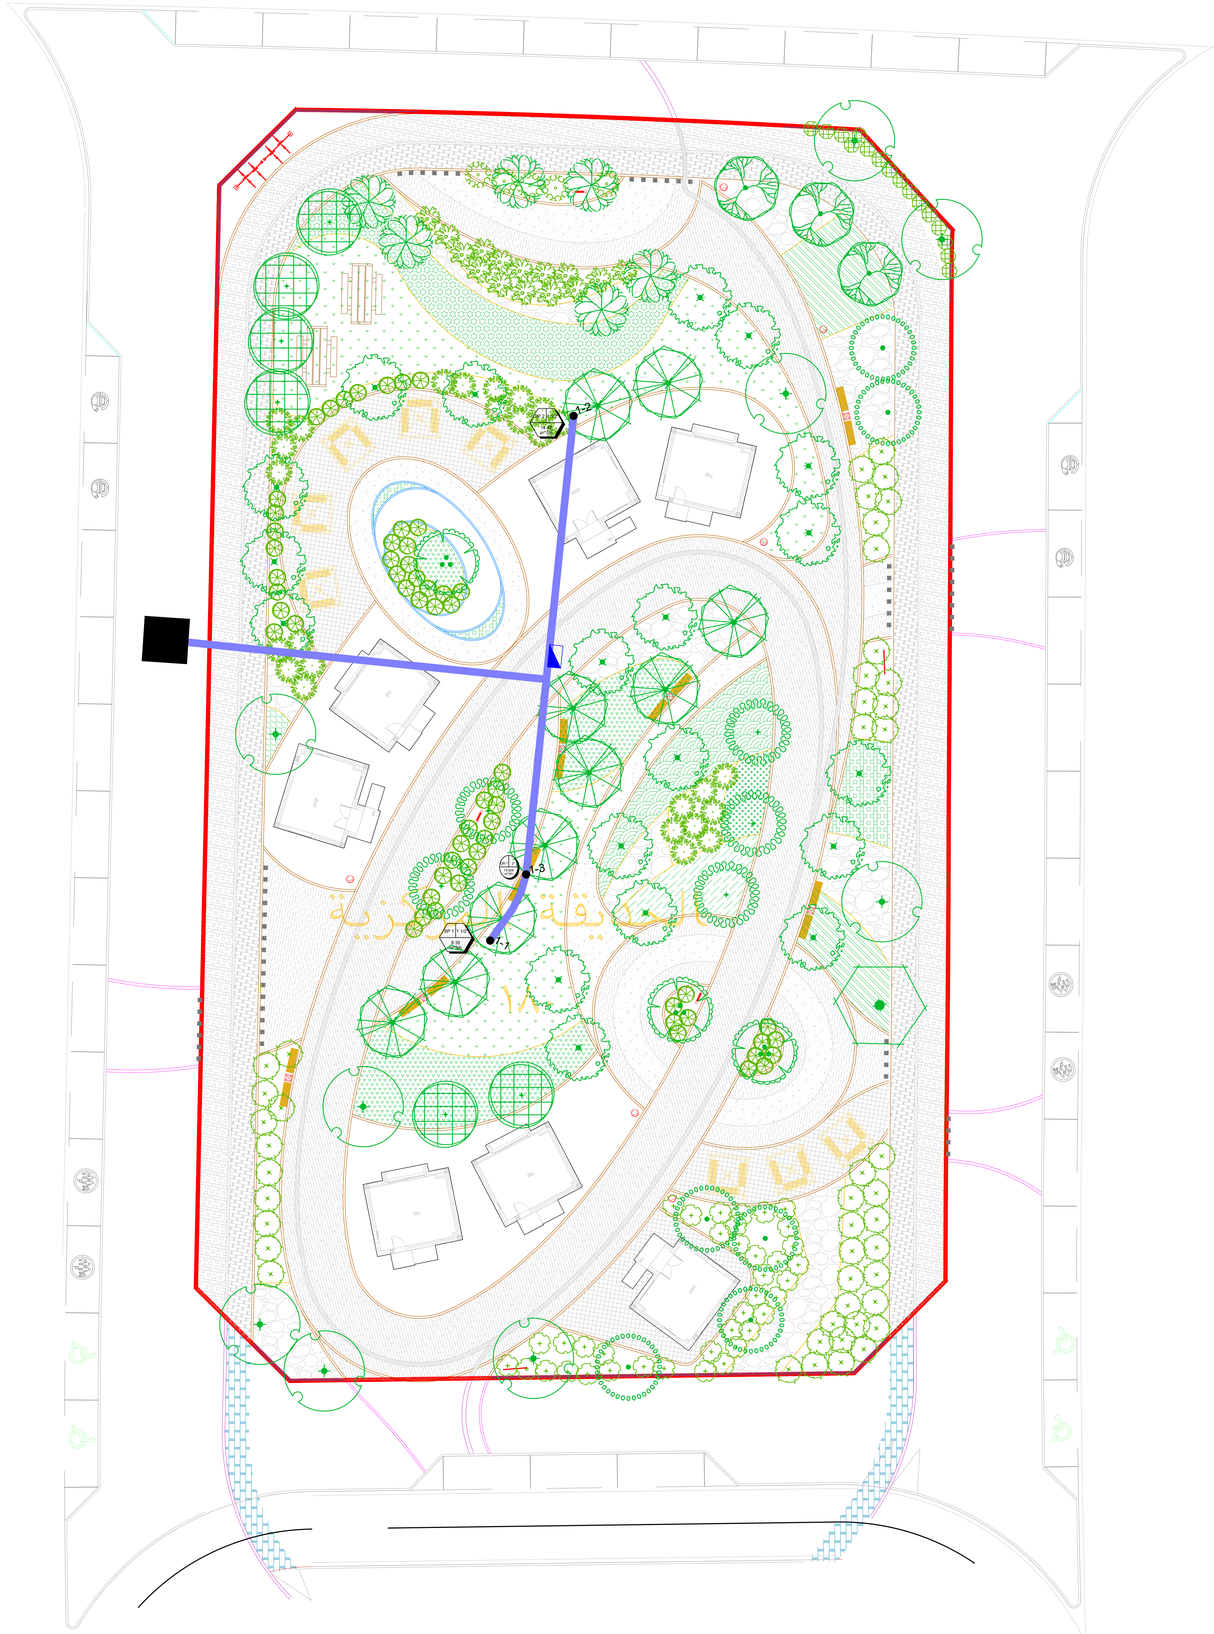

PROJECT NAME : Sample Soft
LOCATION : CAIRO,EGYPT

KEY PLAN :

LEGEND :

Irrigation

Qty	Symbol	Description	Part #
2	●	Rain Bird 150PESB-R	150PESB-R
1	●	Rain Bird 200PESB-R	200PESB-R
1	■	New Water Source	
69 (m)	▬	Irrigation Cables	
1	◢	Controller	ESP-TM2-4

LOGO :

NOTES :

DRAWING NAME : Design of Irrigation Valve Cables Layout

DRAW BY : TAREK MOSTAFA

CHACKED BY : KAREEM HESHAM

DATE : 00 / 00 / 2026

SCALE : N.T.S.

DRAWING ON : 01 REV 00

CODE :

A	B	C	D