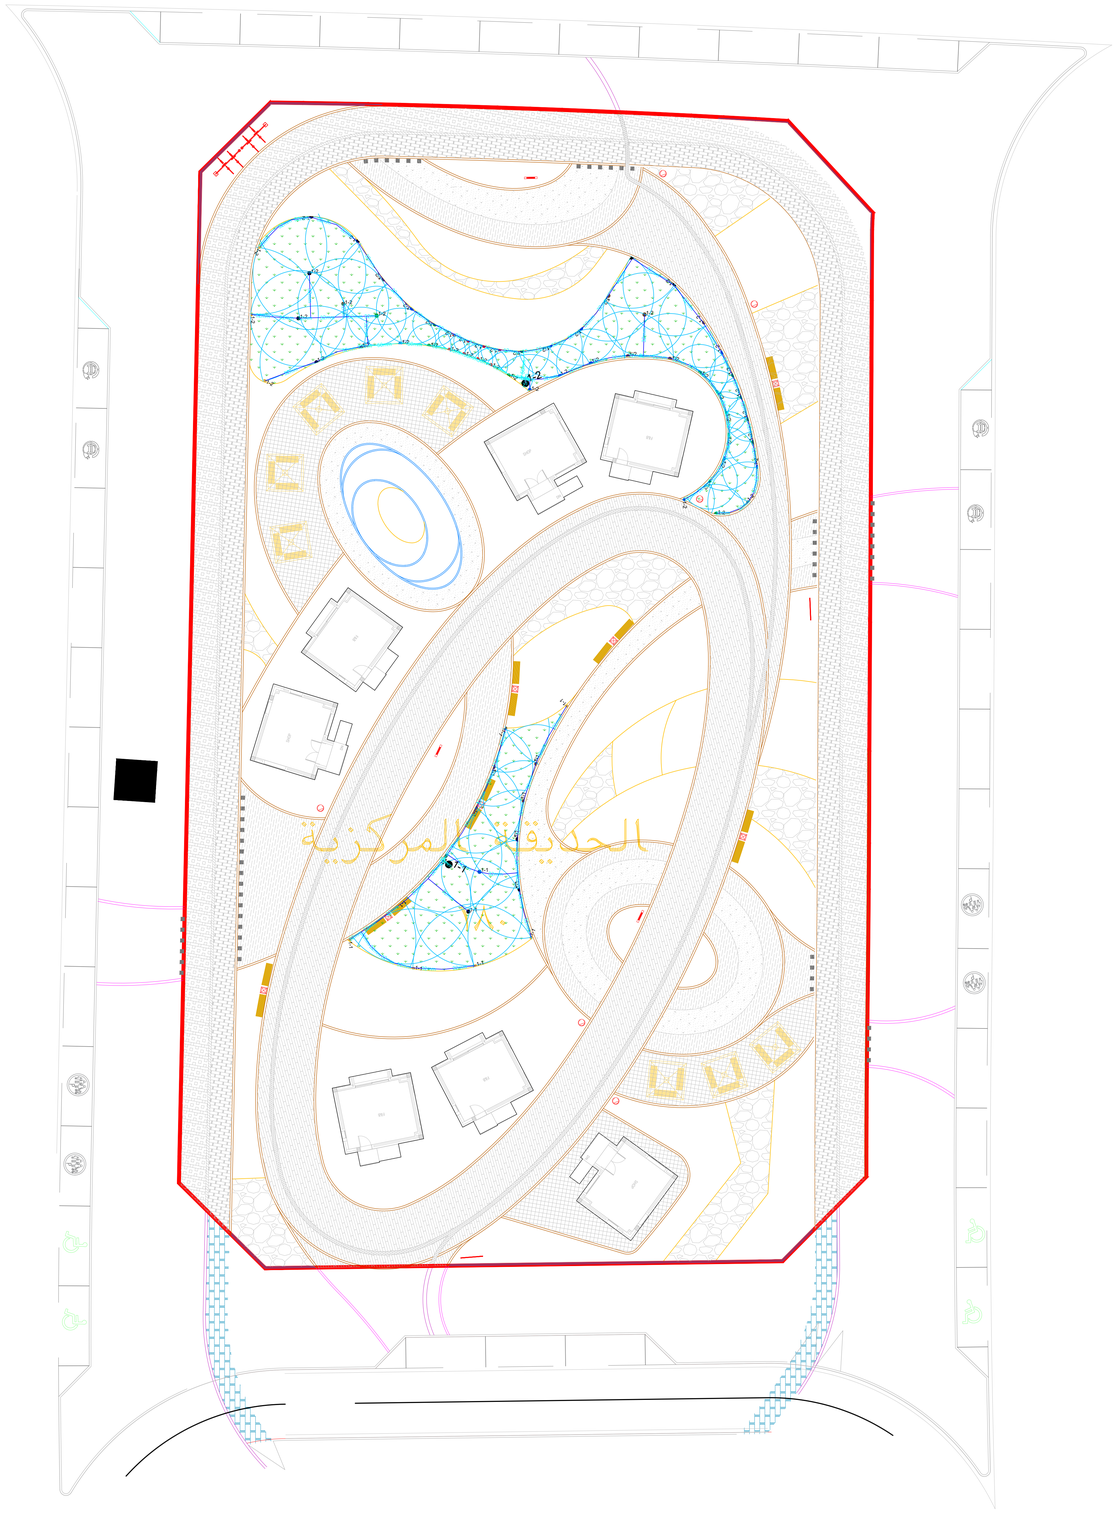

PROJECT NAME : Sample Soft
LOCATION : CAIRO,EGYPT

KEY PLAN :

LEGEND :

Irrigation

Qty	Symbol	Description	Part #	Pressure	Flow	Radius
8		Rain Bird MPR-5H - 1804-PRS	MPR-5H	2.1	0.05	1.5
5		Rain Bird HE-VAN-08 180 - 1804-PRS	HE-VAN-08	2.1	0.13	2.4
9		Rain Bird HE-VAN-08 270 - 1804-PRS	HE-VAN-08	2.1	0.2	2.4
1		Rain Bird HE-VAN-08 360 - 1804-PRS	HE-VAN-08	2.1	0.27	2.4
4		Rain Bird HE-VAN-10 180 - 1804-PRS	HE-VAN-10	2.1	0.21	3.1
6		Rain Bird HE-VAN-10 270 - 1804-PRS	HE-VAN-10	2.1	0.31	3.1
1		Rain Bird HE-VAN-10 360 - 1804-PRS	HE-VAN-10	2.1	0.41	3.1
1		Rain Bird HE-VAN-10 90 - 1804-PRS	HE-VAN-10	2.1	0.1	3.1
3		Rain Bird HE-VAN-12 180 - 1804-PRS	HE-VAN-12	2.1	0.27	3.7
9		Rain Bird HE-VAN-12 270 - 1804-PRS	HE-VAN-12	2.1	0.4	3.7
2		Rain Bird HE-VAN-12 360 - 1804-PRS	HE-VAN-12	2.1	0.54	3.7
4		Rain Bird HE-VAN-15 180 - 1804-PRS	HE-VAN-15	2.1	0.42	4.6
3		Rain Bird HE-VAN-15 270 - 1804-PRS	HE-VAN-15	2.1	0.63	4.6
3		Rain Bird HE-VAN-15 360 - 1804-PRS	HE-VAN-15	2.1	0.84	4.6
1		Rain Bird HE-VAN-15 90 - 1804-PRS	HE-VAN-15	2.1	0.21	4.6
5		Rain Bird 18-VAN 180 - 1804-PRS	18-VAN	2.1	0.61	5.5
1		Rain Bird 18-VAN 270 - 1804-PRS	18-VAN	2.1	0.91	5.5
3		Rain Bird 18-VAN 90 - 1804-PRS	18-VAN	2.1	0.3	5.5
2		Rain Bird 150PESB-R	150PESB-R			
1		New Water Source				
184.76 (m)		Lateral - 32mm				
16.61 (m)		Lateral - 50mm				
0.39 (m)		Lateral - 63mm				
0.39 (m)		Lateral - 75mm				

LOGO :

NOTES :

DRAWING NAME : Sprinkler Irrigation Design Layout

DRAW BY : TAREK MOSTAFA

CHACKED BY : KAREEM HESHAM

DATE : 00 / 00 / 2026

SCALE : N.T.S.

DRAWING ON : 01 REV 00

CODE :

A	B	C	D