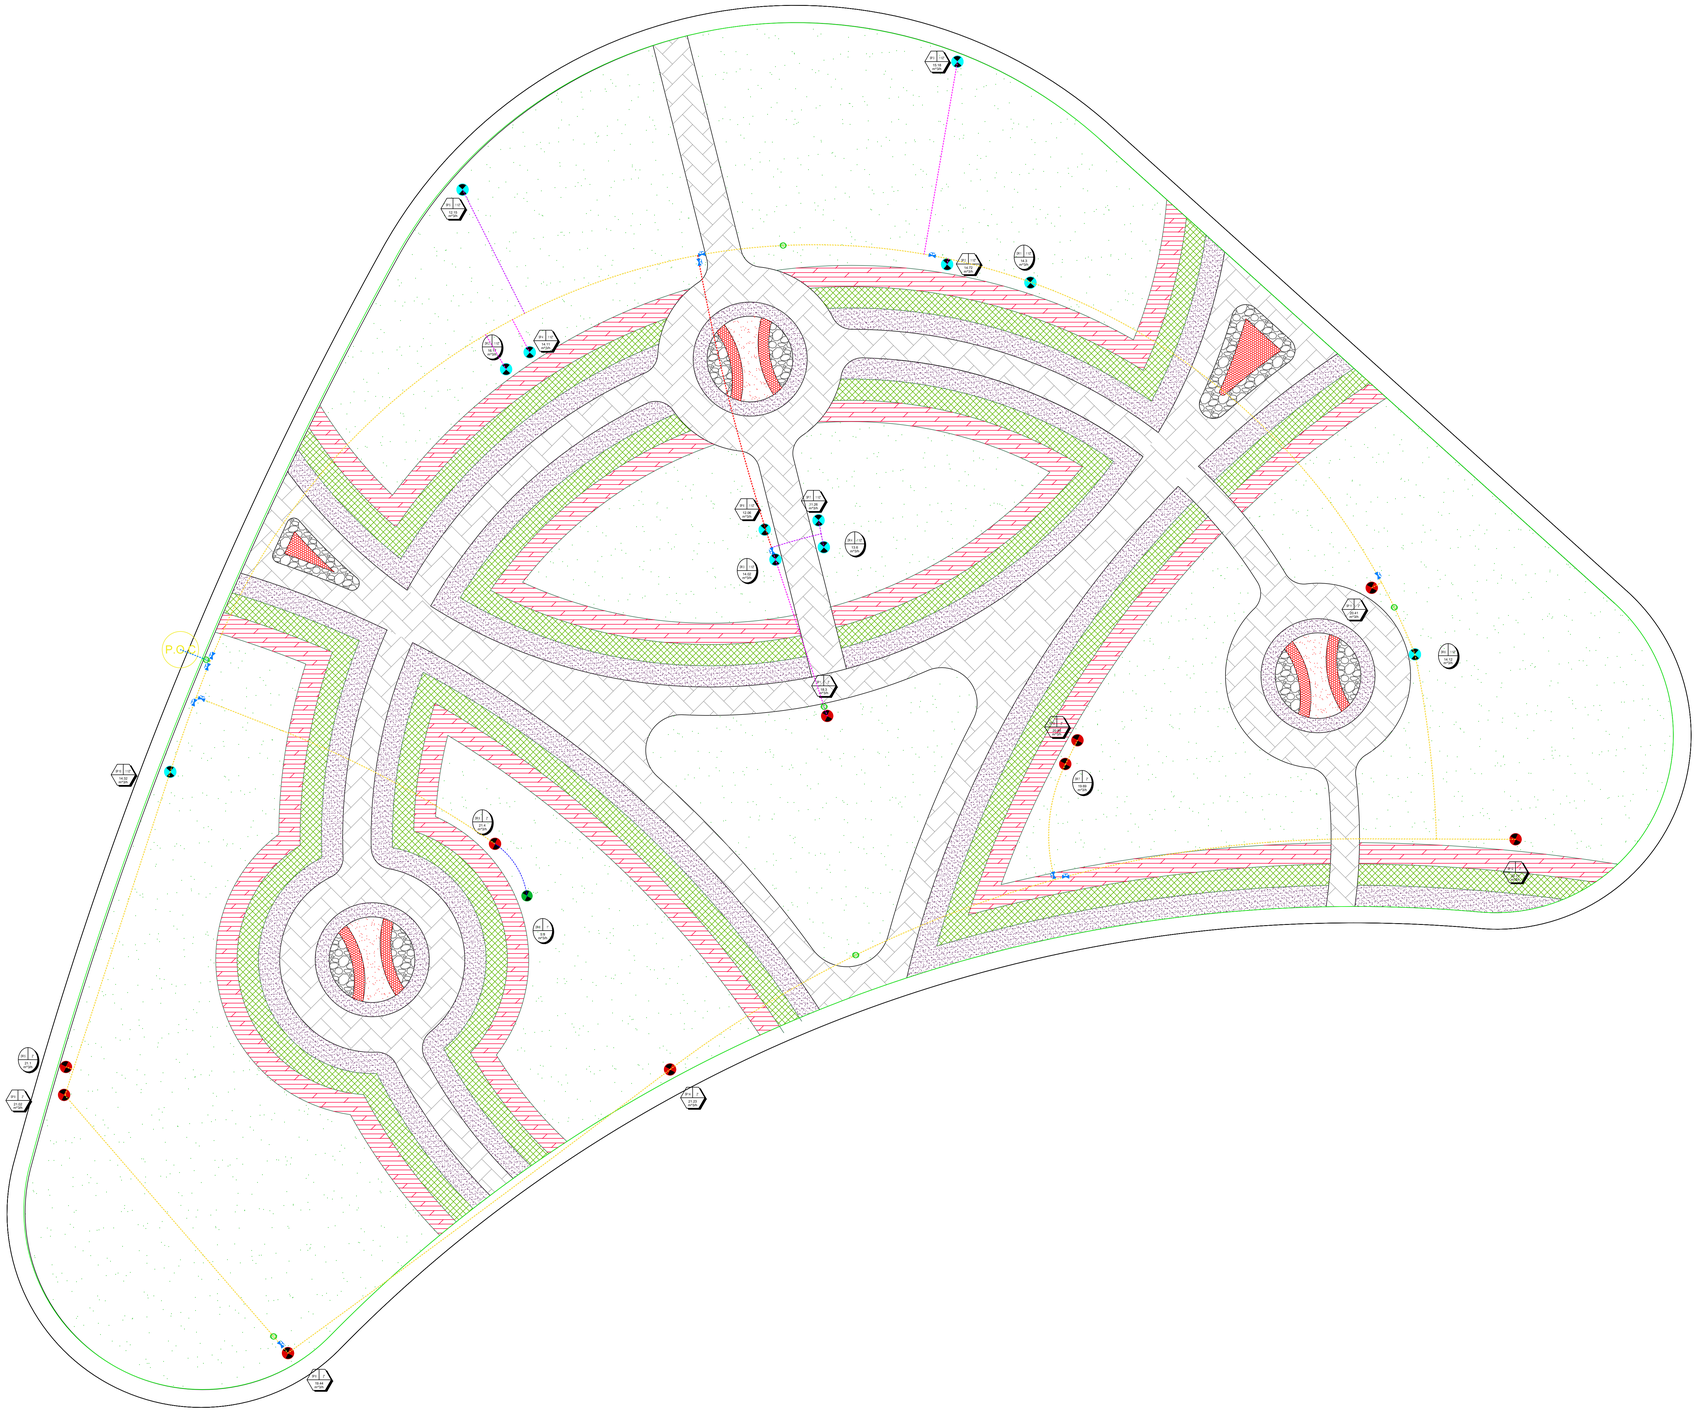

PROJECT NAME : larg project
LOCATION : GIZA,EGYPT

KEY PLAN :

LEGEND :

Si.	Symbol	Name	QTY.	Unit
1		Valve Spray 2" inch	10	no.
2		Valve Spray 1.5" inch	12	no.
3		Valve Spray 1" inch	1	no.
4		Isolation Valve	12	no.
5	C	Q.C.Valve	6	no.
6		Pipe 32 mm	9	m
7		Pipe 63 mm	31	m
8		Pipe 75 mm	65	m
9		Pipe 90 mm	621	m
10		Pipe 110 mm	43	m
11		Pipe 160 mm	5	m

LOGO :

NOTES :

DRAWING NAME : The Main Line of Irrigation Network Design

DRAW BY : TAREK MOSTAFA

CHACKED BY : KAREEM HESHAM

DATE : 11 / 1 / 2025

SCALE : N.T.S.

DRAWING ON : 01 REV 00

CODE :

A	B	C	D