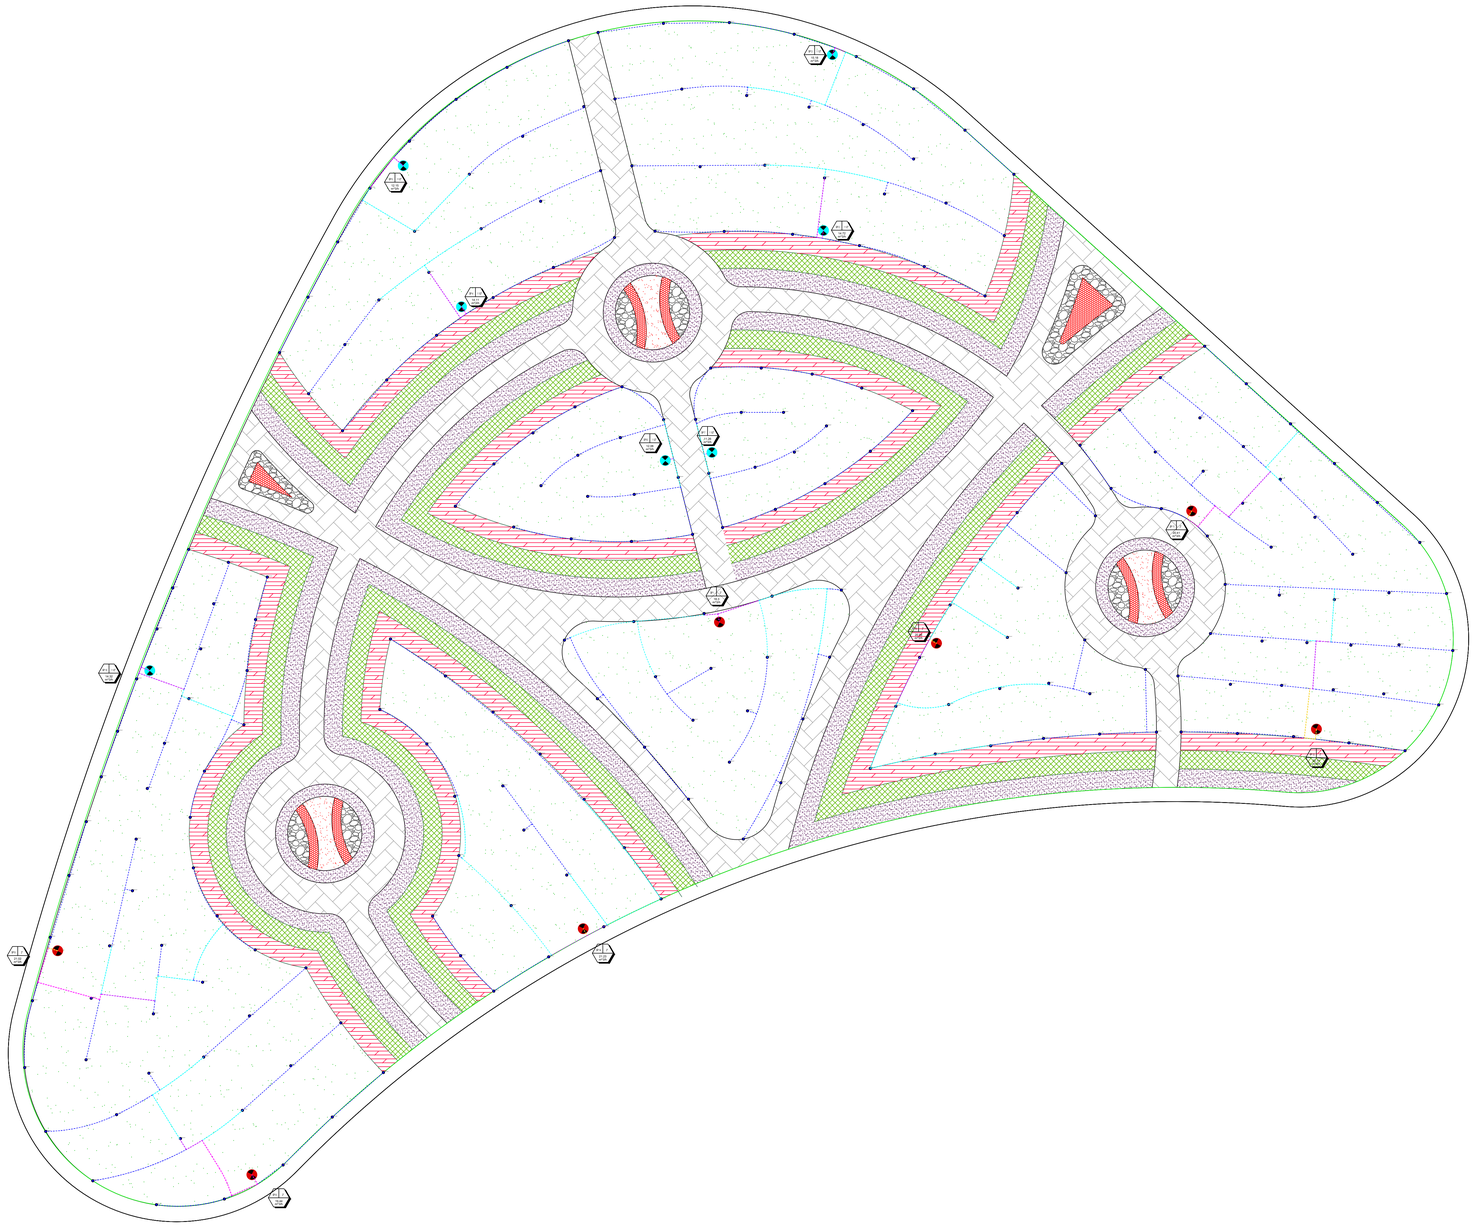

PROJECT NAME : larg project
LOCATION : GIZA,EGYPT

KEY PLAN :

LEGEND :

Si.	Symbol	Name	QTY.	Unit
1	MPR 25 Q	MPR 25 Q	3	no.
2	MPR 25 H	MPR 25 H	4	no.
3	MPR 25 F	MPR 25 F	15	no.
4	MPR 30 Q	MPR 30 Q	4	no.
5	MPR 30 H	MPR 30 H	39	no.
6	MPR 30 F	MPR 30 F	49	no.
7	MPR 35 Q	MPR 35 Q	16	no.
8	MPR 35 H	MPR 35 H	76	no.
9	MPR 35 F	MPR 35 F	34	no.
10		Valve Spray 2" inch	7	no.
11		Valve Spray 1.5" inch	7	no.
12		Pipe 32 mm	1439	m
13		Pipe 50 mm	382	m
14		Pipe 63 mm	101	m
15		Pipe 75 mm	45	m
16		Pipe 90 mm	18	m

LOGO :

NOTES :

DRAWING NAME : Sprinkler Irrigation Design Layout

DRAW BY : TAREK MOSTAFA

CHACKED BY : KAREEM HESHAM

DATE : 27 / 12 / 2024

SCALE : N.T.S.

DRAWING ON : 01 REV 00

CODE :

A	B	C	D